

АРХИТЕКТУРА СССР

ЕЖЕМЕСЯЧНЫЙ ЖУРНАЛ

ОРГАН ГОСУДАРСТВЕННОГО КОМИТЕТА
ПО ГРАЖДАНСКОМУ СТРОИТЕЛЬСТВУ
И АРХИТЕКТУРЕ ПРИ ГОССТРОЕ СССР
И СОЮЗА АРХИТЕКТОРОВ СССР

№ 6 1968. Год издания XXXV

СОДЕРЖАНИЕ

Б. Рубаненко, В. Шквариков, Ю. Бочаров, Е. Кутырев	Проблемы планировки и застройки города Тольятти	1
М. Вайнберг, Е. Крашенинникова	Определение целесообразных сроков реконструкции жилого района крупного города	14
Б. Колотилкин	К вопросу разработки теории надежности зданий и сооружений	22
Г. Агранович, Н. Скулачева	Архитектура стенок строительных заводов	25
Д. Шерман	Архитектурно-планировочные прин- ципы проектирования заводских сто- ловых	31
Д. Масленников	Теория ошибок при графоаналитиче- ских расчетах инсоляции помещения	35
И. Орлов	Галерейные жилые дома для южных районов страны	38
Д. Готман, Ю. Дыховичный, Н. Никитин, А. Румянцев, Б. Щепетов	Проектирование и строительство общественных зданий и сооружений нуждается в коренном улучшении	45
М. Грекина	Наталья Борисовна Чмутина	47
Д. Бабаян	Анна Тиграновна Тер-Аветикян	47
	Каким должно быть подмосковное село	48
А. Яничкин	В Государственном комитете по гражданскому строительству и архи- тектуре при Госстрое СССР	49
А. Лейкина	В Союзе архитекторов СССР	50
С. Моисеева	Пленум правления Союза архитекторов Узбекистана	51
М. Евсеева	ВДНХ. Юбилейная экспозиция «Ленинград»	52
С. Тутученко, М. Барановский	Сооружения на туристских маршру- тах в Польше	54
В. Куйбышев	Олимпийский комплекс в Гренсбле	59

Проблемы

Авторский коллектив ряда научно-исследовательских и проектных институтов работает над проектом планировки и застройки города Тольятти¹.

В наше время — время развернутого строительства коммунизма — особенно важно, чтобы планировка и застройка новых городов соответствовали современным и перспективным социальным требованиям, предъявляемым к организации труда, быта и отдыха населения, отличались высокими техническими и архитектурно-планировочными качествами и, вместе с тем, обеспечивали бы возможность постепенного удовлетворения все возрастающих потребностей населения города. В связи с этим необходимо было четко, на высоком научном уровне определить программные требования к генеральному плану и разработать мероприятия, обеспечивающие создание нового города — здорового, удобного и красивого.

Программа формирования генерального плана нового города рассматривалась как перспективная программа его развития на 2000-й год и далее, как пример органического сочетания генерального плана города с задачами первой очереди строительства, т. е. с проектами детальной планировки и застройки, рассчитанными на 1971—1975 годы. Эти проекты опираются на пятилетние планы развития народного хозяйства города, в которых разработаны требования комплексного решения вопросов жилищного строительства, культурно-бытового обслуживания, инженерного оборудования, озеленения и внешнего благоустройства.

В разработанную программу входили: определение научно обоснованного взаиморазмещения производственных зон, селитебных образований и озелененных пространств;

¹ Авторский коллектив: архитекторы Б. Р. Рубаненко, В. А. Шквариков (руководители), А. М. Базилевич, Ю. П. Бочаров, Е. Л. Нохелес, К. К. Карташова, Е. И. Кутырев, М. Д. Липовецкая, А. С. Образцов, В. А. Плинер, М. К. Савельев; инженеры А. А. Агасьянц, Л. М. Блинкова, С. М. Воронин, Н. А. Дыховичная, Г. А. Каплан, Г. П. Кормер, Т. А. Кузнецова, М. В. Сельская, В. П. Сельянов, И. Я. Стирис, В. А. Токатлы, В. П. Ходатаев.



планировки и застройки города Тольятти

правильное размещение, организация и застройка промышленных районов на специально выделенных территориях города, с учетом группового размещения предприятий, максимального их кооперирования между собой, особенно в части инженерного оборудования, транспорта, энергоснабжения и складского хозяйства;

определение типов жилых и общественных зданий как для первоочередной, так и перспективной застройки города. На основе выработанной градостроительной типологии зданий была поставлена задача преобразовать строительную базу города Тольятти с учетом возможности возведения зданий повышенной этажности, их градостроительной маневренности и многообразия архитектурно-композиционного решения отдельных зданий, а также застройки жилых районов, магистралей, площадей, набережных и т. д.;

повышение удобств и обеспечение высокого уровня обслуживания населения путем создания гибкой структуры селитебных территорий с учетом развития социальной организации жизни населения в жилом районе и микрорайоне;

обеспечение безопасности передвижения населения путем надежной изоляции пешеходов от транспорта и особенно от скоростного транзитного. Создание условий для организации удобных и быстрых транспортных связей с наименьшей затратой времени на трудовые передвижения;

создание системы открытых и озелененных пространств, обеспечивающих организацию отдыха и занятия спортом;

обеспечение прогрессивным инженерным оборудованием и внешним благоустройством городских территорий.

При разработке новой планировочной структуры города Тольятти мы исходили из того положения, что новый город следует рассматривать не изолированно, а только в системе расселения, так как между населенными местами будут крепнуть устойчивые производственные, культурно-бытовые и другие связи. Эти связи в значительной мере будут определять планировочную структуру нового города: его размеры, характер промышленной застройки, размещение селитебной территории, транспортные связи и т. п.

Поэтому генеральный план развития города и проект планировки его пригород-

ной зоны разрабатывались одновременно, в полной органической взаимосвязи.

В ЦНИИЭП жилища и ЦНИИП градостроительства был создан единый коллектив проектировщиков и научных работников, последовательно решавших все проблемы: от общей концепции расселения населения и размещения производства до разработки комплексов жилых и общественных зданий, отдельных сооружений и элементов благоустройства нового города.

Был создан и успешно реализован общий план работы 17 научно-исследовательских и проектных институтов для выпуска проектной документации по различным отраслям городского хозяйства (головной институт — ЦНИИЭП жилища). В работе участвуют ведущие организации Госкомитета по гражданскому строительству и архитек-

*Б. РУБАНЕНКО,
В. ШКВАРИКОВ,
Ю. БОЧАРОВ,
Е. КУТЫРЕВ*

Схема района размещения города. Вариант 1 — существующие населенные пункты; 2 — проектируемая площадка города Тольятти



туре, Госстроев СССР и РСФСР, МКХ РСФСР, Министерства здравоохранения СССР, Министерства просвещения и др.

При разработке генерального плана новой части города Тольятти предусмотрено: единое функциональное и архитектурно-пространственное решение новой и ранее сложившейся части города Тольятти и возможность их включения в более крупную градостроительную систему в качестве относительно законченных и взаимосвязанных комплексных звеньев планировочной структуры крупной агломерации;

качественное преобразование планировочной структуры городов и дальнейшее пропорциональное развитие всех его важнейших зон при максимальной концентрации жилищно-гражданского и промышленного строительства и законченности на каждом этапе строительства;

возможность развития новых функциональных зон, в первую очередь, научно-исследовательских институтов, зон высших учебных заведений, научно-технических и деловых учреждений;

формирование законченного современного облика города с учетом композиционной роли промышленной архитектуры и идейно-художественной значимости важнейших общественных комплексов при выразительной и разнообразной жилой застройке и обеспечении доминирующей роли водных пространств и массивов зеленых насаждений во всей композиции города;

сочетание преимущественного развития массового пассажирского транспорта с повышенной нормой индивидуальных автомашин (200 машин на 1000 жителей) и включение новейших транспортных устройств и сооружений в структуру города.

Участок строительства нового города Тольятти расположен примерно в середине треугольника, образуемого городами Куйбышев, Сызрань и Мелекес на расстоянии от них от 70 до 90 км. Территория города расположена на обширной равнине вдоль северного берега водохранилища Волжской ГЭС им. В. И. Ленина, между двумя крупными лесными массивами против Жигулевских гор и устья реки Усы, в 5—7 км к западу от сложившейся части города Тольятти. Под строительство новой части города отведено около 8 тыс. га на наиболее благоприятных в санитарно-гигиеническом и архитектурно-композиционном отношении территориях, примыкающих к берегу водохранилища и лесу, с учетом возможности дальнейшего развития города в западном и северном направлениях.


Проектная численность населения новой и существующей частей города составит на 1975 г. — 390 тыс. и на 2000 г. — 500 тыс. человек. При расчете трудовых кадров учтены перспективы широкого внедрения автоматики, повышение уровня культурно-бытового обслуживания и связанное с этим увеличение до 22—25% удельного веса работников коммунального хозяй-

ства, торговли, просвещения и других обслуживающих отраслей.


При определении перспектив развития города было учтено его благоприятное экономико-географическое положение, которое позволит кооперировать новые предприятия с промышленностью Куйбышевской области и прилегающих районов. Учтено размещение города вблизи крупных железнодорожных автомобильных и водных коммуникаций, а также наличие мощной энергетической базы — Волжской ГЭС им. В. И. Ленина.

На стадии генерального плана проведено моделирование процесса формирования города и складывающейся на его основе агломерации рассмотрены основные варианты возможного взаимного расположения функциональных зон и сопоставлены условия расселения при различных схемах пространственного роста города.

Одной из важнейших задач следует считать решение генеральной структурной схемы развития города Тольятти как в пределах, так и за пределами условного расчетного срока генерального плана (к 2000 г. и далее). Методика этой работы основана на выборе главного направления пространственного роста города за его расчетные размеры, выявлении значительных резервов малоценных для сельского хозяйства территорий, на моделировании процесса развития важнейших зон, определении параметров и очередности строительства комплексных звеньев структуры города.

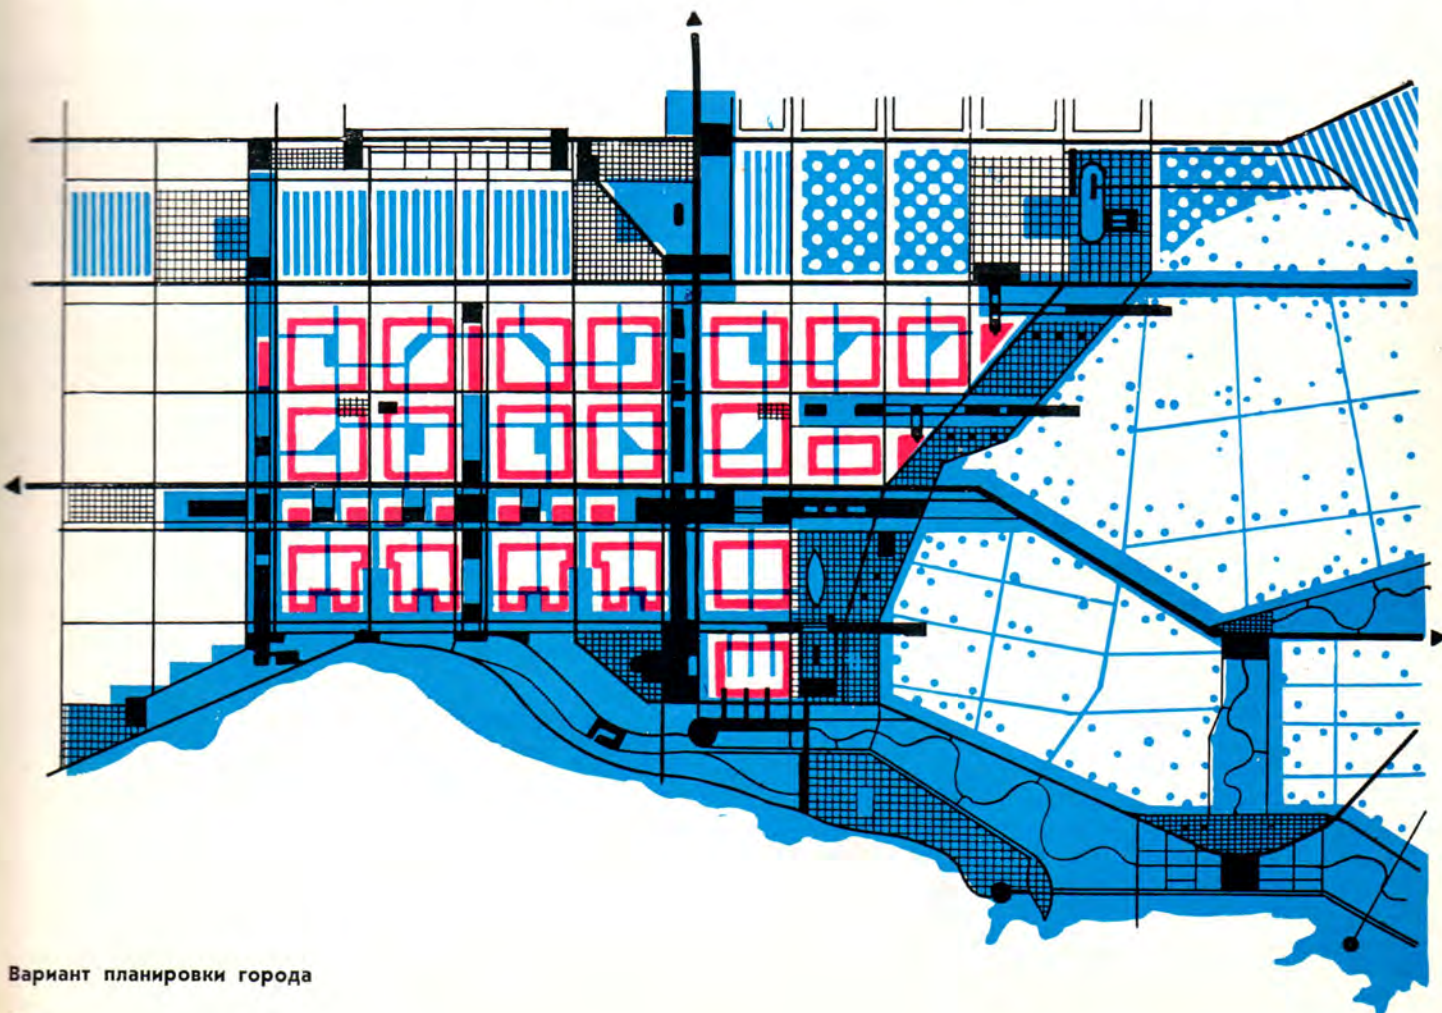

Вариант планировки города

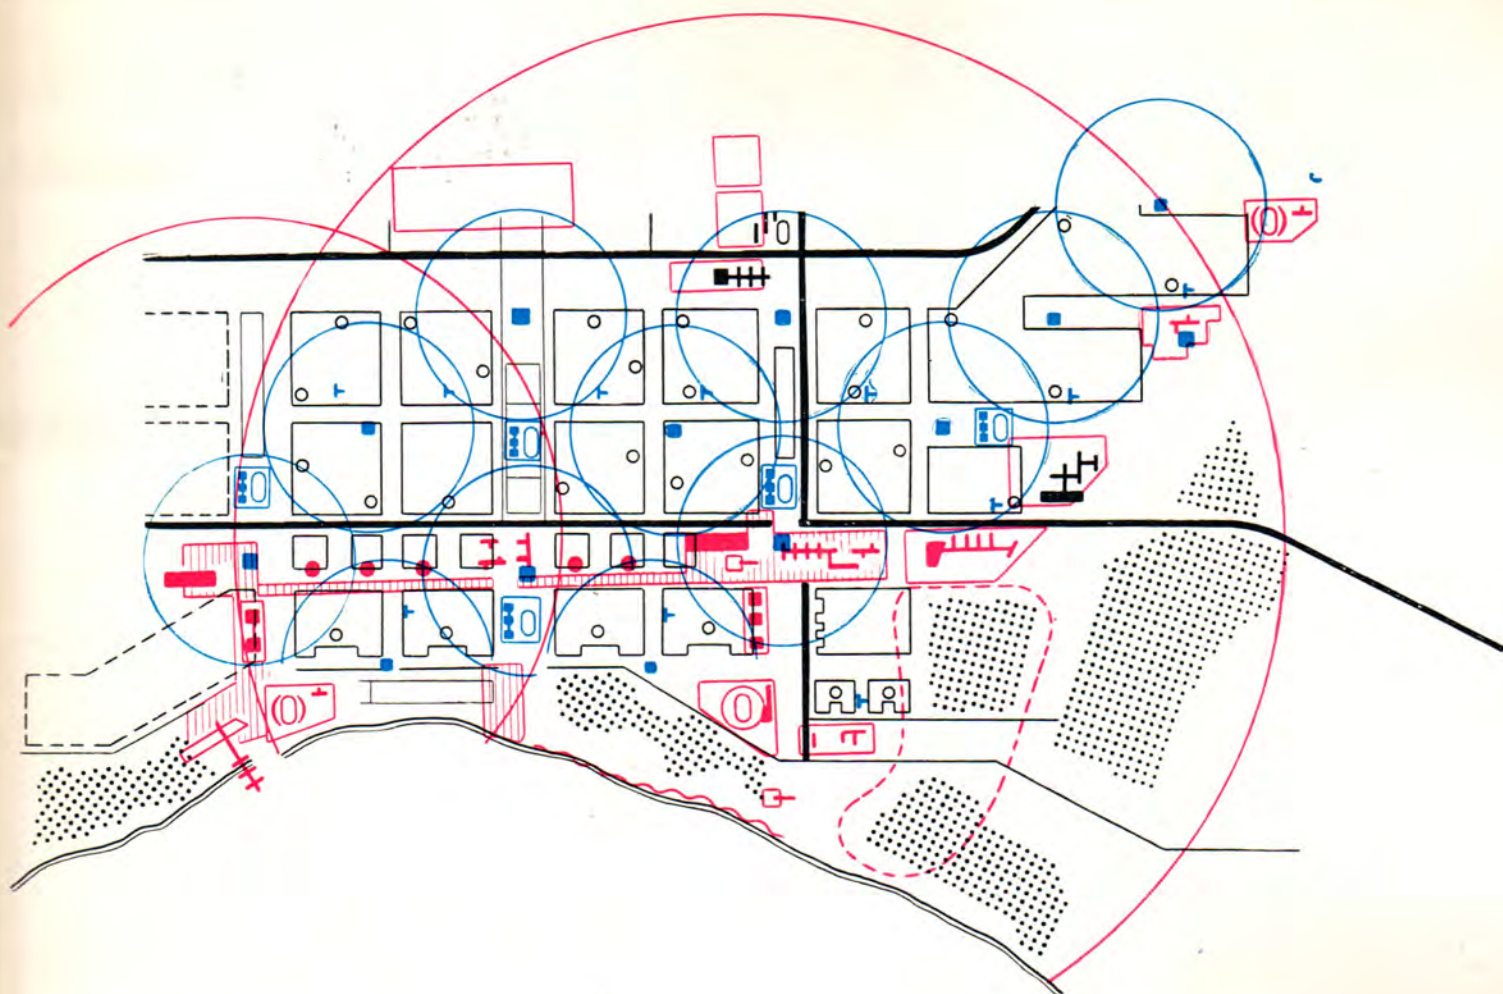

- Общественный центр микрорайона
- Подцентр жилого района
- Горгово-культурный центр жилого района
- Спортивный центр жилого района
- ⊥ Поликлиника жилого района
- ⊥ Административный центр городского района
- ⊥ Спортивный центр городского района
- ⊥ Гостиница
- ⊥ Дворец пионеров

- Зона городского центра
- Торговый центр города
- ⊥ Культурный центр города
- Клубы
- ⊥ Административный центр города
- ⊥ Деловой центр города
- ⊥ Медицинский центр с медучилищем
- ⊥ учебный центр автозавода

- ⊥ Общегородской учебный центр
- ⊥ Культурный и спортивный комплекс учебного центра
- ⊥ Научный центр (НИИ автомобильной промышленности)
- ⊥ Общегородской спортивный центр
- ⊥ Яхт-клуб
- ⊥ Территория пляжа и зона отдыха
- ⊥ Парк культуры и отдыха

Необходимо было также дать оценку природных факторов, оказавших существенное влияние на пространственную организацию города.


В структурной схеме города выявлены направления освоения территорий основных функциональных зон (промышленных, селитебных, транспортных, мест загородного отдыха, зон научных и учебных заведений). В результате были установлены основные направления территориального роста города.

В целях рациональной организации труда, быта и отдыха населения в проекте предусмотрено создание функциональной и структурной целостности и законченности города на каждом основном этапе его строительства, предусмотрена возможность дальнейшего взаимоувязанного развития важнейших районов, обеспечена ведущая роль нового района в структуре всего города.

При решении пространственной организации города использованы прогрессивные

Схема организации культурно-бытового обслуживания

принципы создания гибкой планировочной структуры, обеспечивающей возможность трансформации функциональных зон с сохранением устойчивых связей между ними в процессе роста города. Характерный для такой структуры территориальный рост городов в одном направлении создает предпосылки для максимального сосредото-

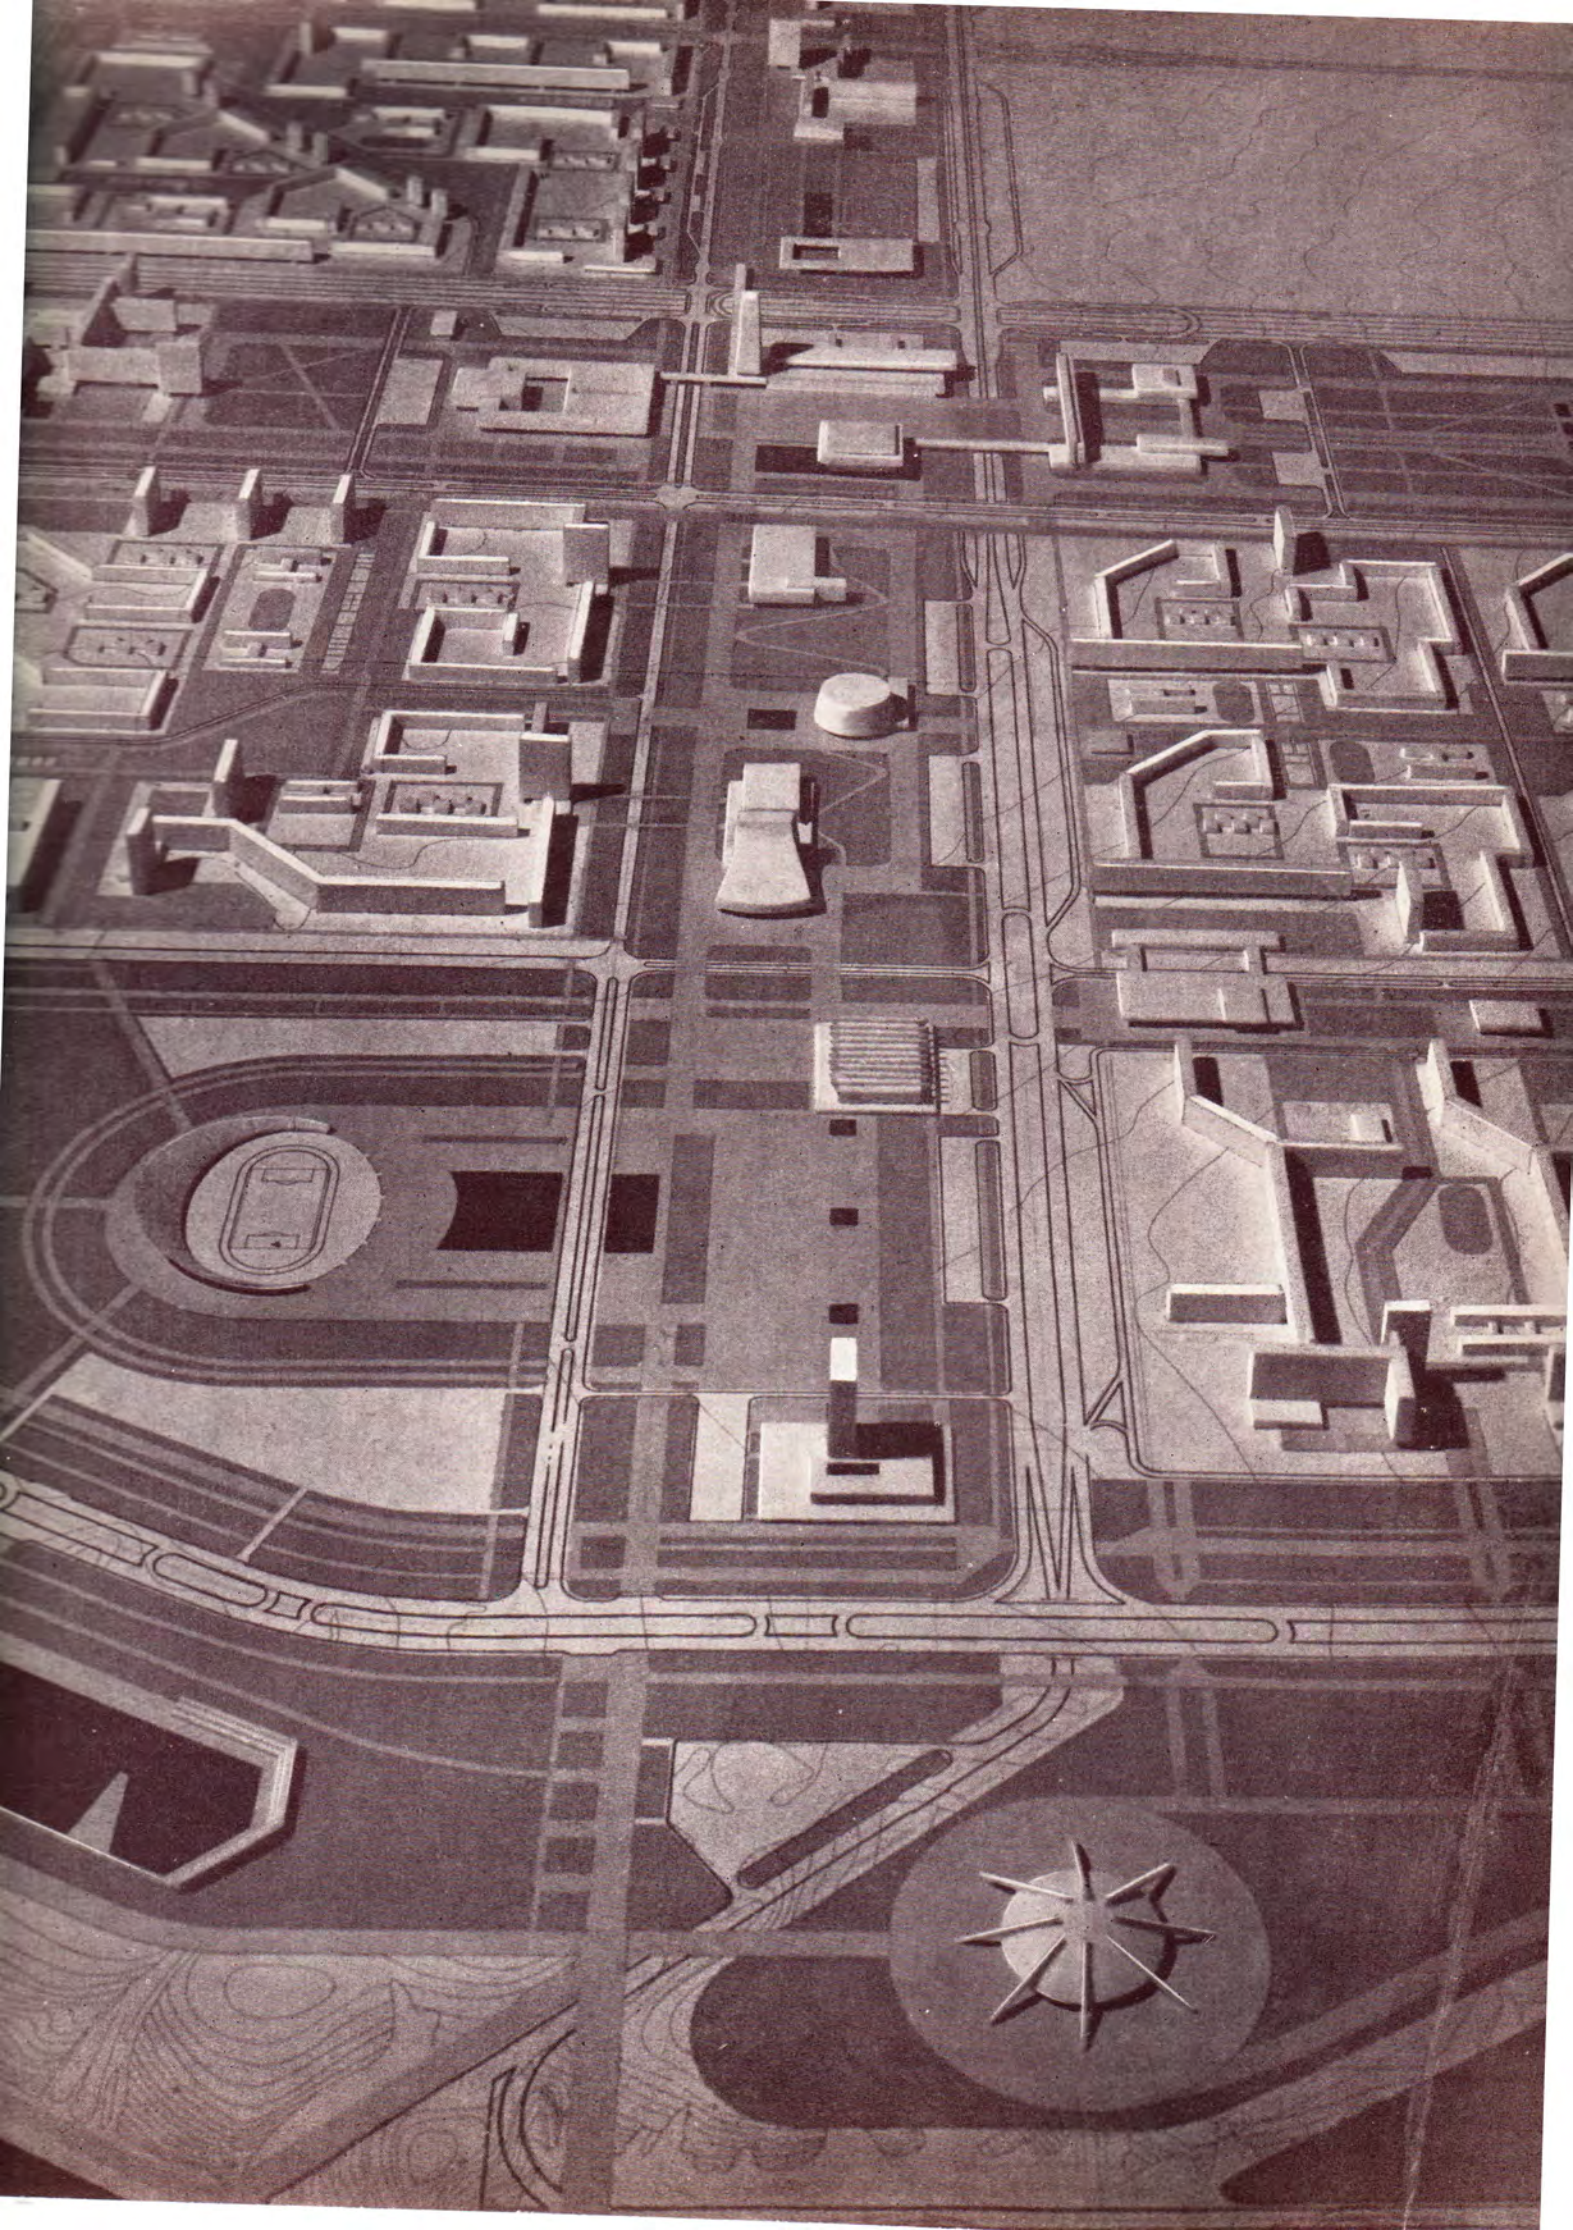

чения строительства в строго ограниченном числе районов, а также для формирования общегородского центра, связанного с районами крупного жилищного и промышленного строительства.

В связи с сокращением рабочего времени одной из важнейших социальных предпосылок формирования современного крупного города является обеспечение полноценного отдыха городского населения как в самом городе, так и за его пределами. Поэтому мы считали необходимым включить в планировочную структуру города крупный лесной массив Гослесфонда СССР. Заповедный лес размером в несколько тысяч гектаров объединяет существующую и новую части города и удобно связан скоростными дорогами со всеми жилыми районами. При этом доступность леса не превышает 25 минут, а для 80 — 100 тыс. человек лес будет расположен в зоне пешеходной доступности.

В архитектурно-планировочном решении города максимально используются благоприятные природные условия района строительства, предусматривается максимальное приближение жилой застройки, центральных площадей и основных общественных сооружений к берегу водохранилища.

В новой части города организуется крупный промышленный район, состоящий из двух комплексов: Волжского автомобильного завода, ТЭЦ и строительной базы и комплекса местной пищевой промышленности и складов, в котором размещаются единые укрупненные коммунальные предприятия для промышленности города. В предзаводской зоне создается высотное здание заводоуправления с вычислительным центром, инженерными корпусами и т. д.

Между промышленным районом и городом создается озелененная зона шириной около 1,5 км, в которую включены питомники зеленых насаждений. Вблизи этой зоны будут расположены научно-технические и учебные центры, функционально связанные с заводом, его административными и инженерными корпусами. Здесь зарезервированы специальные участки для развития в перспективе научно-исследовательских и высших учебных заведений.

Селитебная зона нового города приближена к берегу водохранилища и лесу. Она четко разделена на четыре планировочных района, два из которых предназначены преимущественно для рабочих и специалистов автомобильного завода, третий (восточный) — для трудящихся предприятий существующей части города, четвертый район — резервный.

Каждый городской район с населением

до 100 тыс. жителей имеет центральную продольную зеленую эспланаду, на которой размещаются объекты городского и районного обслуживания, парки, скверы, районные спортивные комплексы, а также специализированные жилые комплексы для молодежи.

Городской планировочный район со средними параметрами 3,5 км × 2,5 км состоит из 4—6 жилых районов, каждый из которых рассчитан на 24 тыс. жителей при 9 м² жилой площади на человека и 18 тыс. жителей при 12 м². Районы ограничены транспортными магистралями с интервалом в 1 км.

Сеть учреждений культурно-бытового обслуживания строится по ступенчатой системе. Все предприятия группируются в зависимости от радиуса обслуживания населения:

центры микрорайонного значения на 12 тыс. жителей (радиус обслуживания 400—500 м);

центры районного значения (торговые и спортивные) на 80 тыс. жителей с радиусом обслуживания 1000—1200 м.

Система учреждений эпизодического пользования состоит из: культурно-административных центров с кинотеатрами, клубами, библиотеками, райсоветами и другими административными учреждениями, центров, призванных осуществлять роль общественных центров городских планировочных районов с населением 110—120 тыс. жителей;

крупных специализированных центров общегородского значения: Дворца пионеров с детской зоной парка и детским теат-


ром; медицинского центра с многопрофильной больницей и медицинским училищем, вузовского городка;

ВТУЗа Волжского автозавода, зоны научно-исследовательских институтов, выставки достижений народного хозяйства и т. п.; городского центра, состоящего из учреждений административно-хозяйственного профиля, предприятий культуры и отдыха. Предусматривается, что в будущем этот центр станет центром всего города Тольятти.

Территория учреждений общегородского центра составляет 50 га. Она распределяется между зонами размещения административно-хозяйственных организаций, торговли, культуры и коммунально-бытового обслуживания. Кроме того, большую площадь занимают спортивный центр города (46—50 га) и зеленые насаждения общественного пользования (скверы, бульвары, эспланады, городские сады непосредственно примыкающие к центру) — 80 га.

Центр города формируется вдоль главных бульваров-эспланад. Вдоль бульвара Восток — Запад размещается основная часть центра. Она состоит из его торговой зоны, зоны зданий общественных и административно-хозяйственных организаций, отдельных культурно-просветительных и коммунально-бытовых учреждений и завершается территорией ВДНХ и специализированным медицинским центром. Вдоль бульвара Север — Юг расположена культурно-просветительная и спортивная зона центра.

Административная площадь города застраивается комплексом зданий советских и партийных организаций, зданиями Дворца

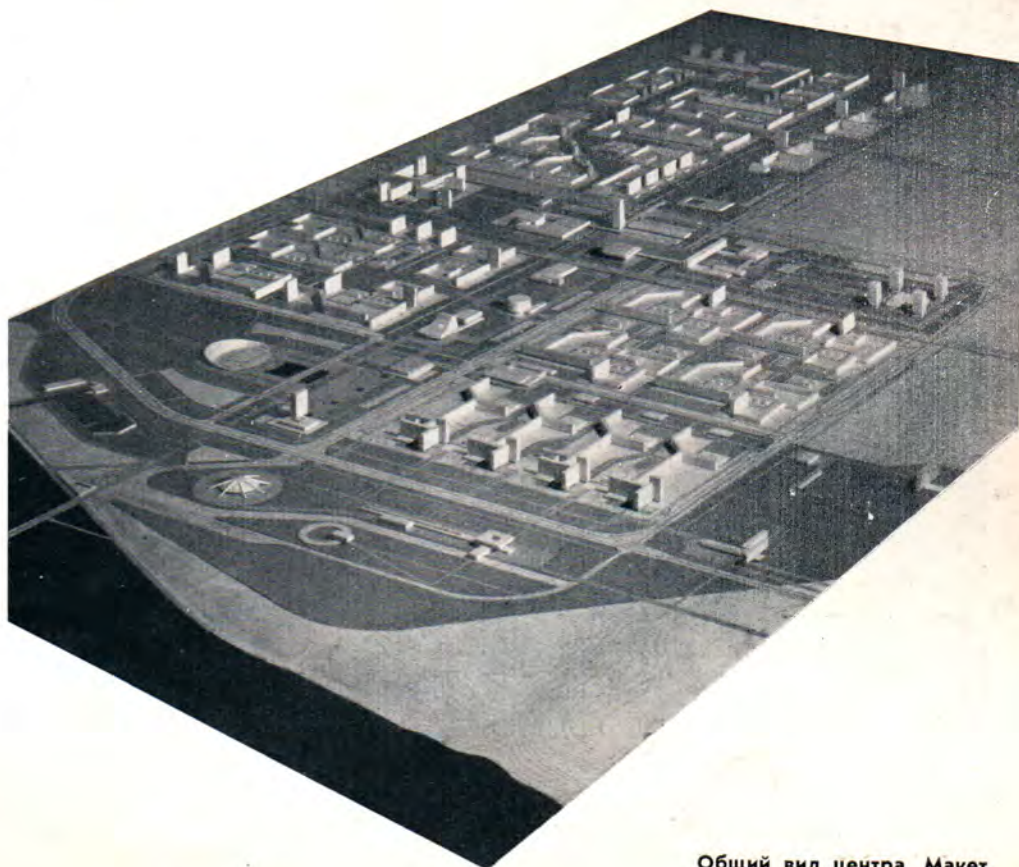

Фрагмент застройки центра

Общий вид центра. Макет

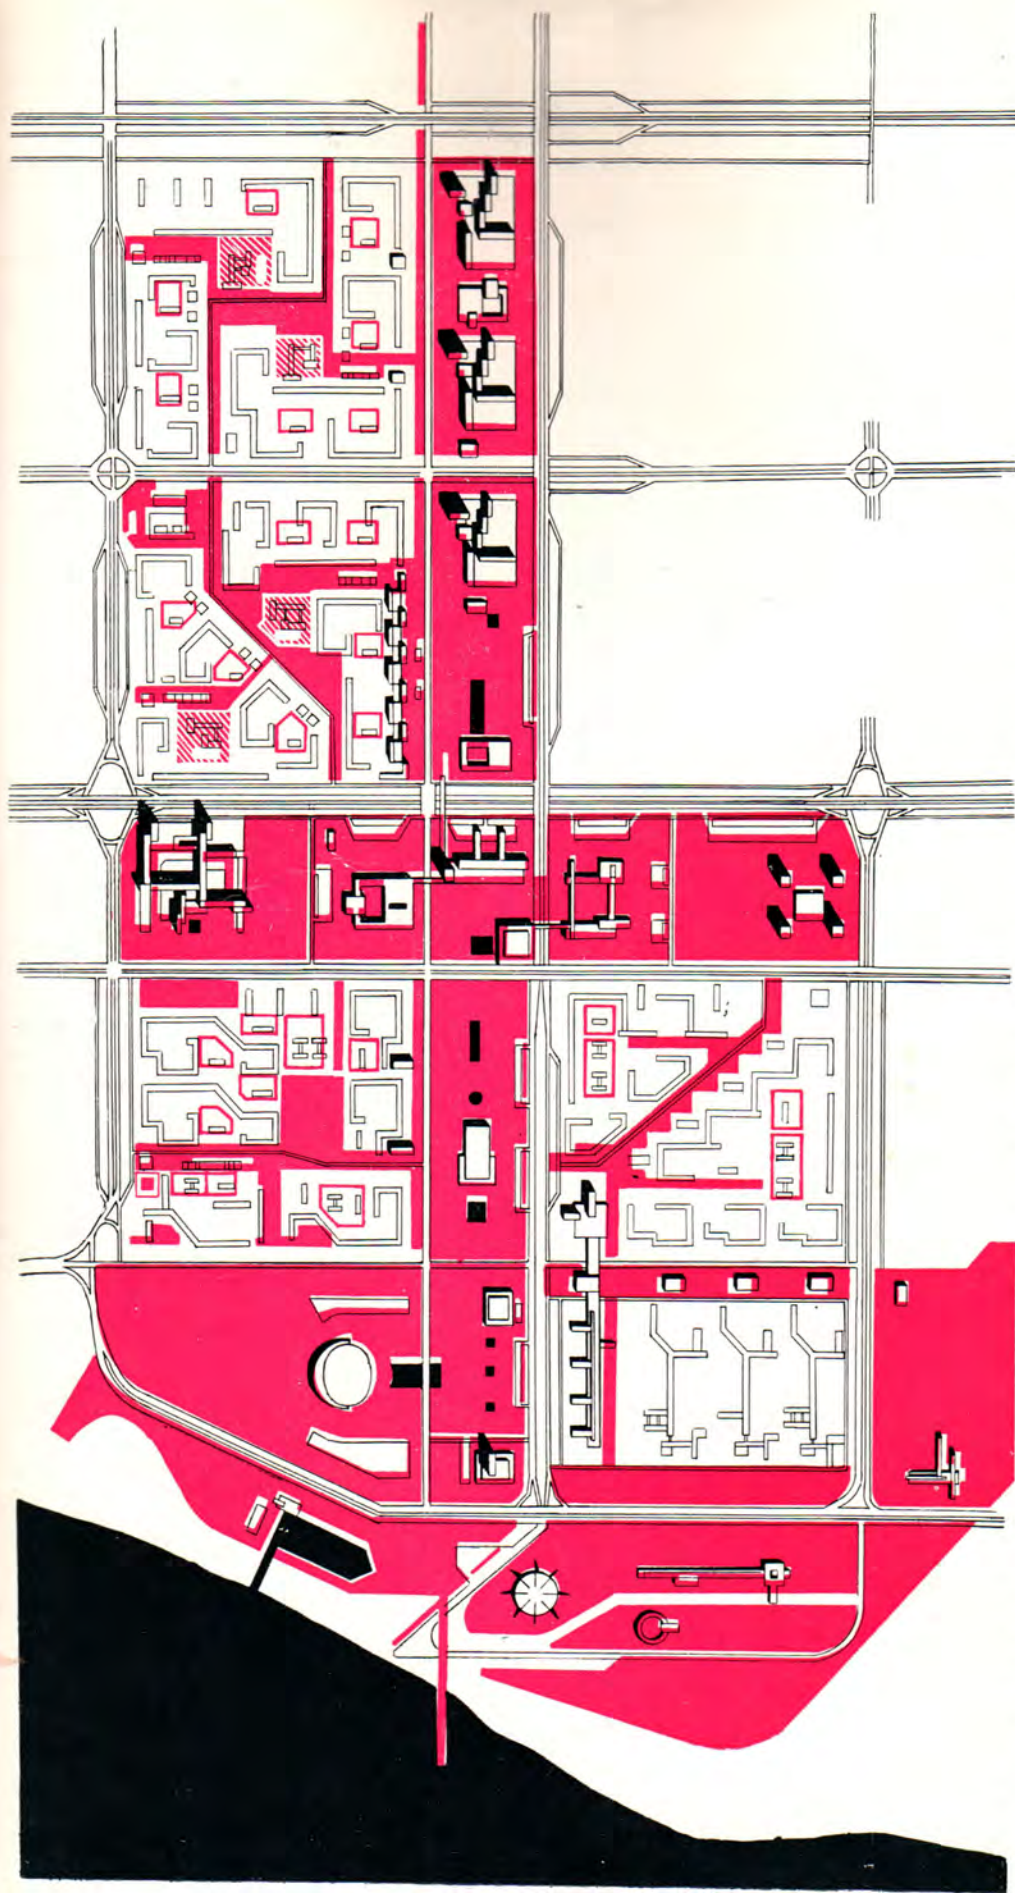


Схема архитектурной композиции центра города

культуры автомобилистов, универсального концертного зала, городской библиотеки и общественно-торгового центра.

На зеленой эспланаде центра размещены драматический театр, дом творческих союзов, цирк, кинотеатр. Эспланада подходит к площади спортивного центра, которая фланкируется зданиями Дворца спорта и 22-этажной гостиницы. Отсюда открывается вид на водохранилище и Жигулевские горы. Секторы прибрежной зоны связаны между собой прогулочной аллеей.

Вдоль берега водохранилища создается развитая, крупномасштабная архитектурно-пространственная композиция, с выделением групп общественных зданий.

Одновременное развитие основных функциональных зон вдоль берега Волги и ориентация главных внешних транспортных связей в направлении север—юг и восток—запад определили планировочную структуру магистральной транспортной сети. Связь между существующей и новой площадками города обеспечивают четыре скоростные дороги. Пропускная способность транспортных магистралей составит примерно 4, а скоростных дорог — 6 тыс. автомашин в час в одном направлении.

Предусматривается создание преимущественно однородных потоков транспорта путем «отвлечения» грузовых и транзитных потоков на городские дороги, проходящие вне селитбы, а движение легкового транспорта — на главную продольную магистраль восток — запад.

Создается комплексный узел внешнего транспорта, состоящий из объединенного железнодорожного и автобусного вокзалов, вертолетной площадки, железнодорожной сортировочной станции и механизированного грузового двора. Реконструируется и расширяется существующий пассажирский и грузовой порт.

По единовременным капитальным затратам, возможностям использования подвижного состава в обычное время суток и простоте организации движения транспорта, а также учитывая перспективное насыщение города легковыми автомобилями в размере 200 автомобилей на 1 тыс. жителей, основным видом городского транспорта принят скоростной автобус. Организацию перевозок трудящихся (до 70% трудящихся от общего количества смены) из жилых районов к заводу и обратно намечается осуществлять экспрессными автобусами. В пределах каждой междомагистральной территории устраиваются 1—2 автобусные станции, связанные диагональными пешеходными дорогами с жилой застройкой.

Для рабочих и инженеров, пользующихся индивидуальным транспортом, устраиваются стоянки в полосе между основной и дублирующей магистралями, проходящей в 120 м от проходных заводов. Для пешеходного и велосипедного движения и город-

Схема озеленения

1 — озеленение площадок детских учреждений и школ; 2 — зелень общественного пользования





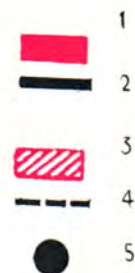


Схема транспортного обслуживания


1 — пешеходные пути; 2 — проезды; 3 — участки общественных зданий; 4 — жилые группы; 5 — гаражи на 150-200 машин

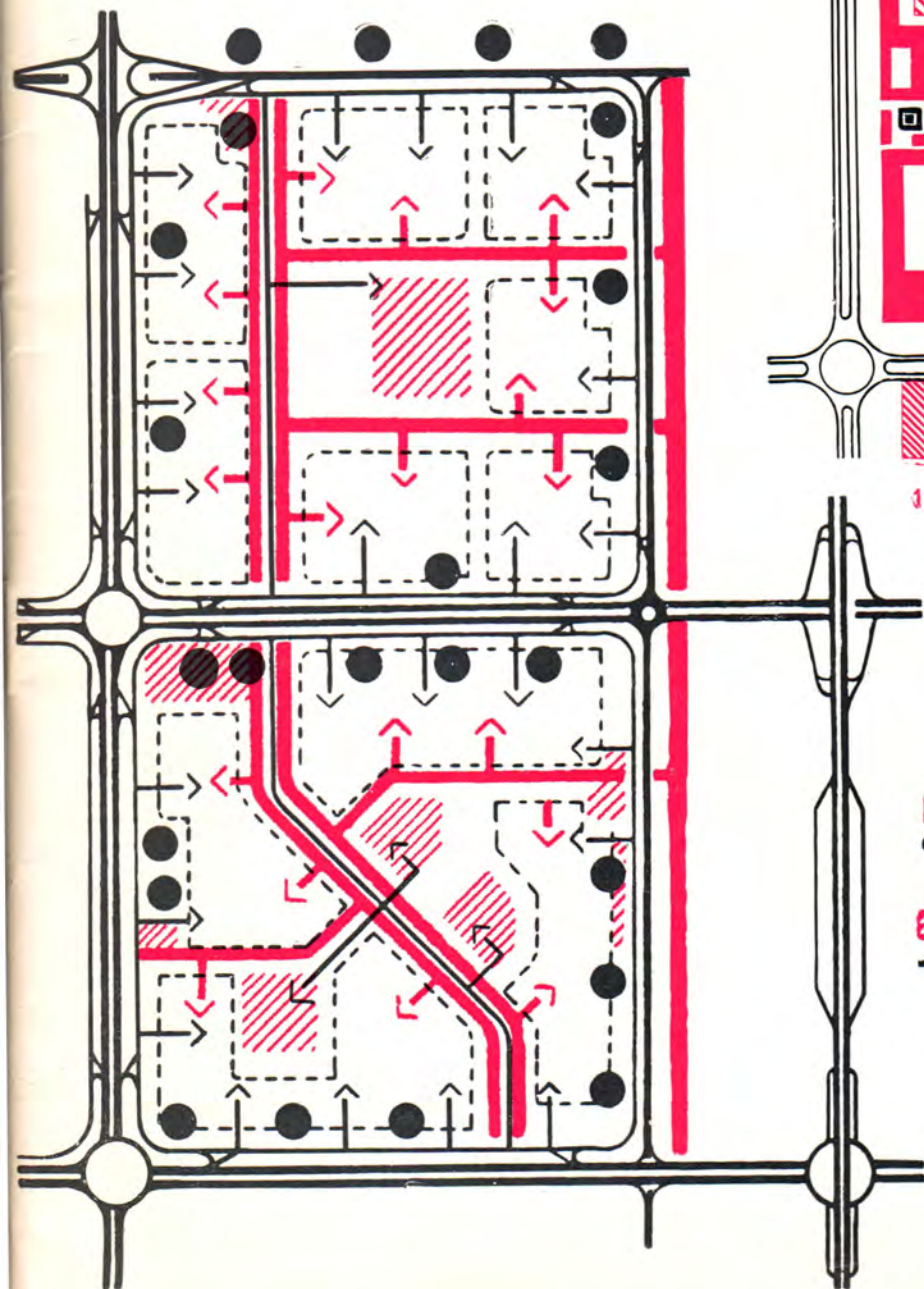
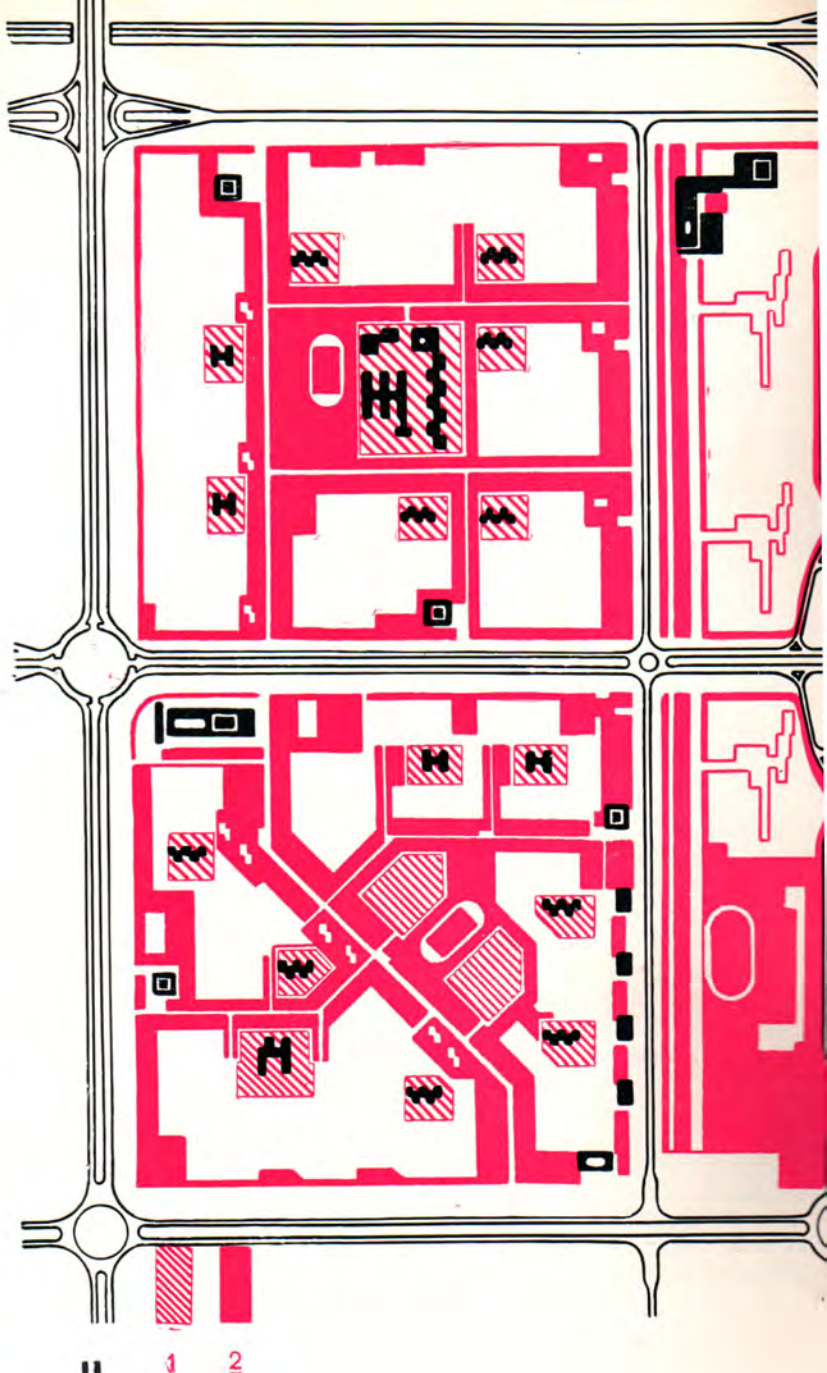
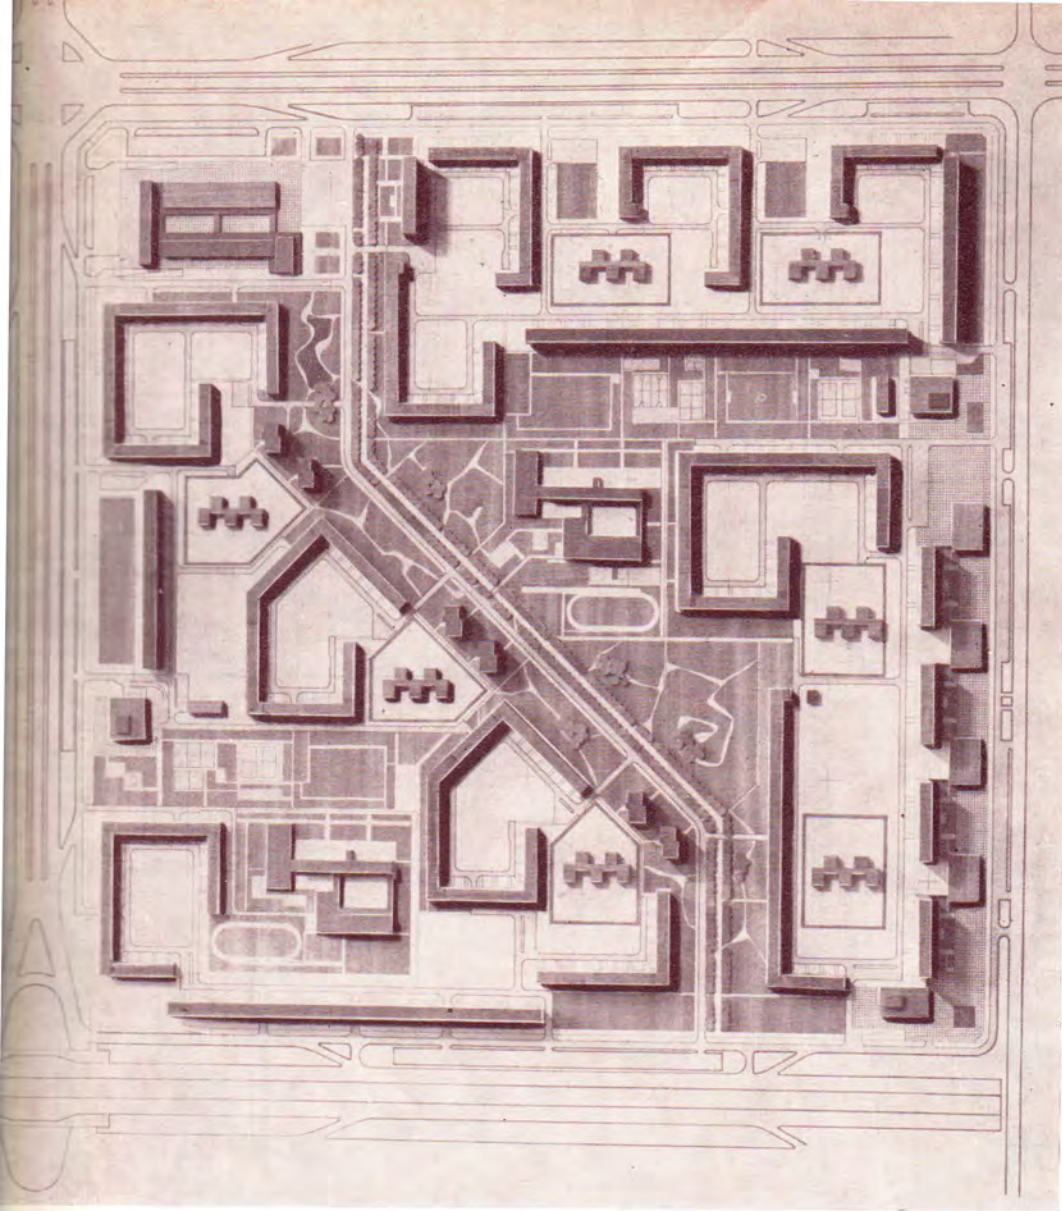


Проект планировки и застройки микро-района 1 очереди строительства

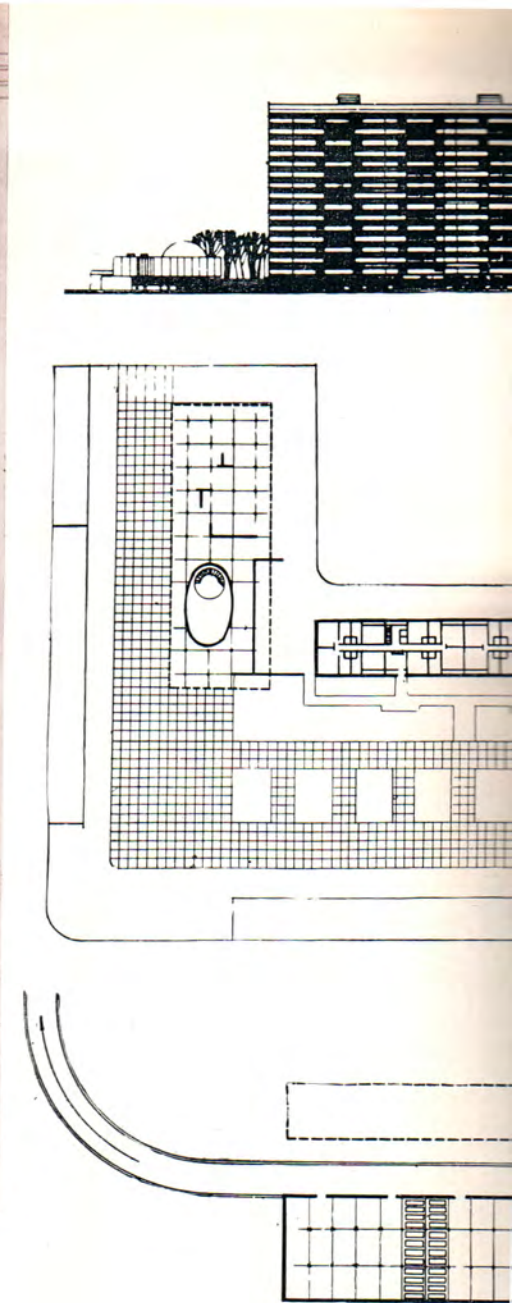

Макет жилого дома

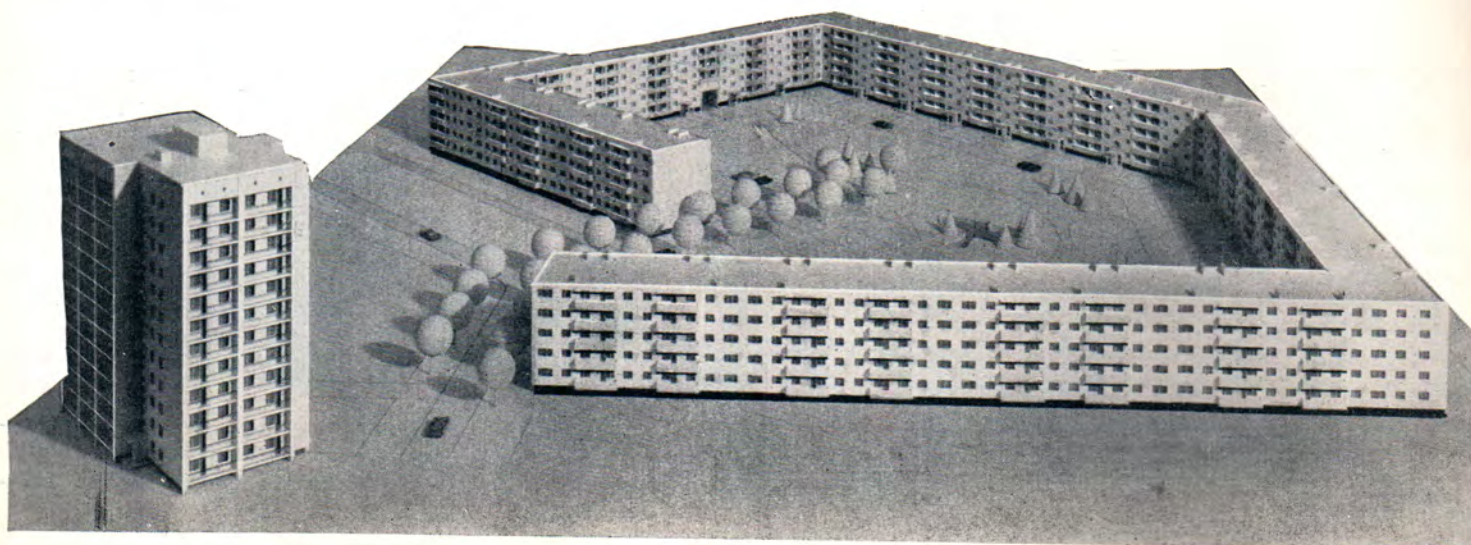


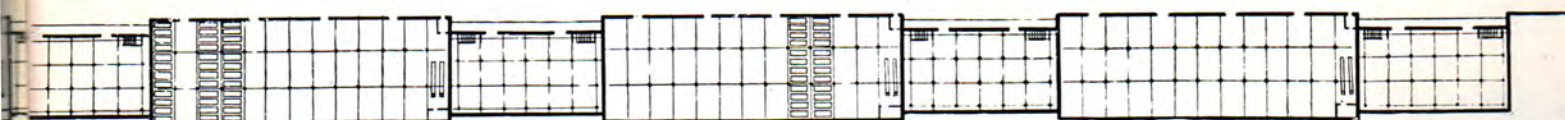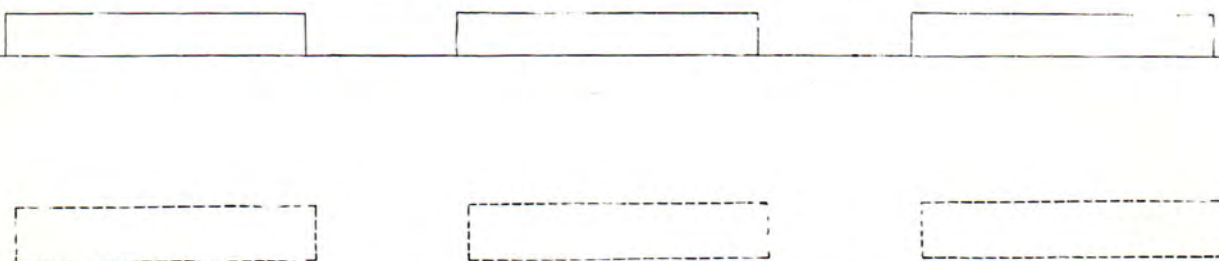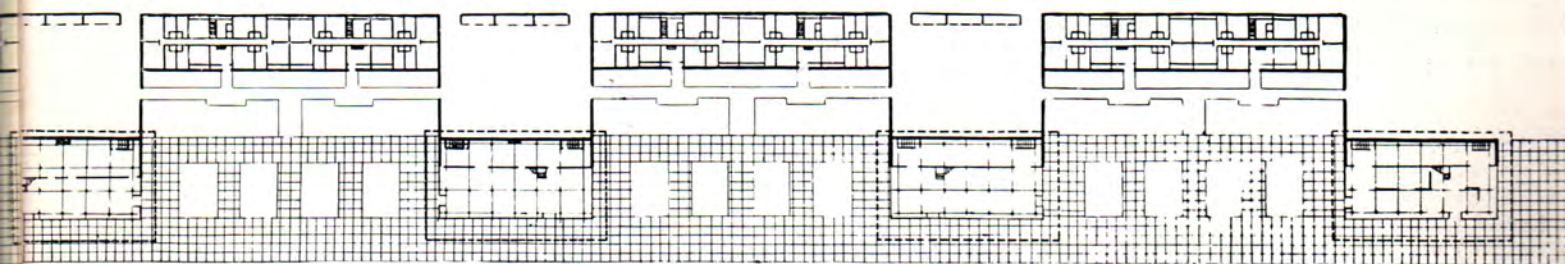

16-этажные крупнопанельные жилые дома
серии П-60. Развертка со стороны Восточ-
ной магистрали, планы первых этажей, под-
валов и разрез


16-этажные крупнопанельные жилые дом
серии П-60



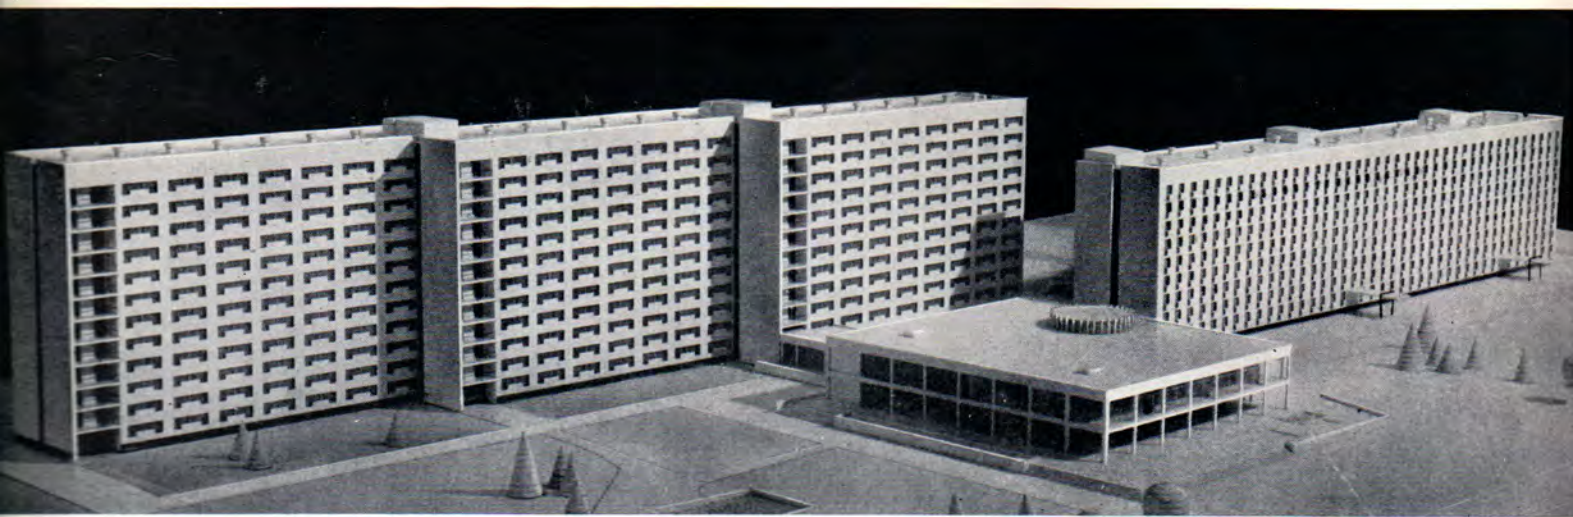

Комплекс жилых домов для малосемейных.

Макет и план

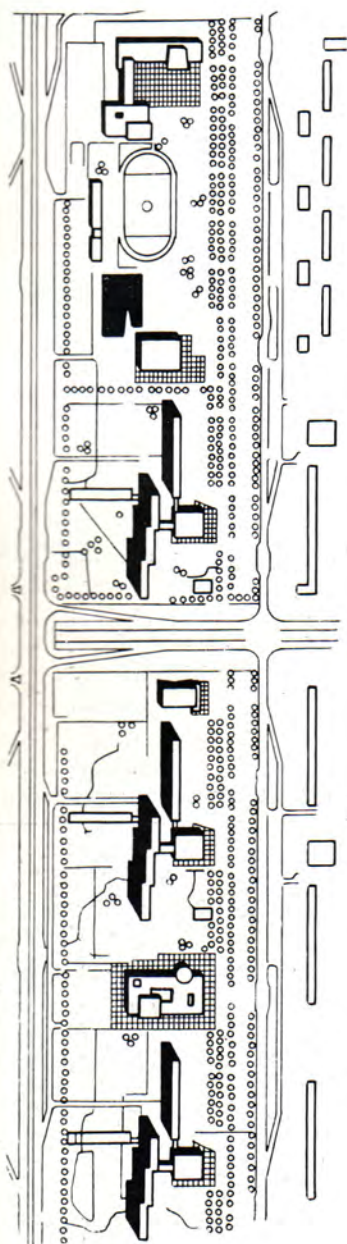

ским транспортом предусмотрены развязки в разных уровнях.


Транспортное решение территории городского центра представляло значительные трудности. Число работающих в центре составляет более 20 тыс. чел., а количество посетителей за сутки превысит 100 тыс. человек.

Транспортное обслуживание центра основывается на построении незамкнутой контурной системы обслуживающих магистралей. Вдоль каждой скоростной магистрали проходит магистраль районного значения, обеспечивающая нормальное функционирование общественного центра города. Центр обеспечивается стоянками до 10 тыс. автомашин с устройством двух-трехэтажных гаражей-стоянок для 20% автомашин.

По генеральному плану намечается организация системы зеленых насаждений общего пользования площадью 750 га из расчета 26 м² на одного жителя. Предусматривается создать «зеленые клинья» от лесного массива, разделяющего существующую и новую части города Тольятти.

включить в эти клинья общегородской парковой зоны, районные сады и бульвары, парк медицинского центра и больницы, сад Дворца пианистов. Будут созданы парки в жилых районах и бульвары в микрорайонах, организованы озелененные защитные полосы, отделяющие промышленную зону от города, ветрозащитные насаждения по фронту водохранилища, а также зеленая зона отдыха и спорта с пляжами, площадками для отдыха вдоль водохранилища. Решение системы зеленых насаждений координируется с системой организации движения пешеходов и транспорта между основными районами города.

Принципы организации первоочередного района нового города являются одними из малоразработанных проблем градостроительства. В то же время принципы решения первого этапа формирования нового города во многом определяют решение генерального плана и направления последующего развития города, существенные

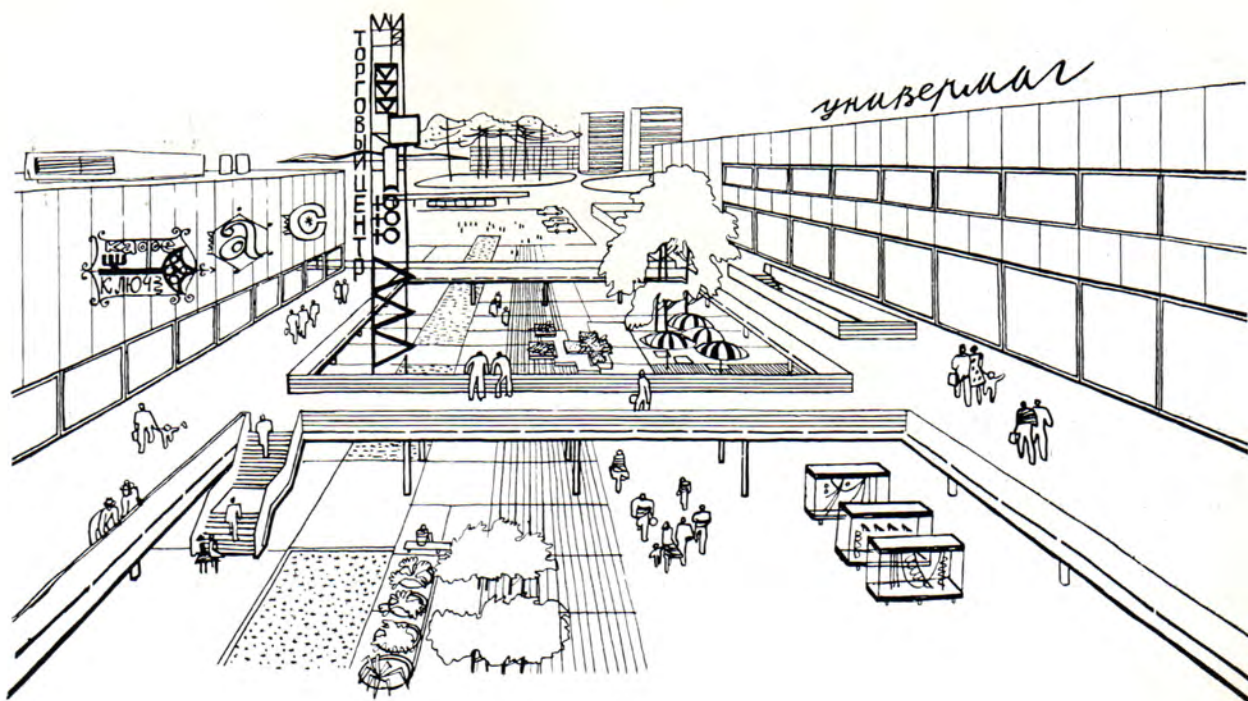

Районный центр. Перспектива

1 — клубные помещения; 2 — райисполком;
3 — молочная кухня; 4 — ресторан; 5 — АТС;
6 — Дом связи; 7 — продовольственный магазин;
8 — милиция; 9 — аптека; 10 — КБО;
11 — суд



Гостиница на 1 тыс. мест


Дворец бракосочетания. Макет

влияют на организацию жизни населения, на экономику строительства и эксплуатацию города, на его архитектурно-пространственную композицию. Опыт показал, что ошибки в планировке первоочередного района значительно осложняют дальнейшее развитие нового города.

Поэтому в генеральном плане особенно большое внимание было уделено первоочередному району строительства и проекту детальной планировки района на 1100 тыс. м² жилой площади, возводимого к моменту пуска Автозавода на полную мощность.

При решении района I-й очереди строительства перед коллективом были поставлены следующие задачи:

обеспечить функциональную и структурную целостность района и создать за сравнительно короткий срок жилой массив с полноценным обслуживанием населения и удобными связями с промышленным комплексом;

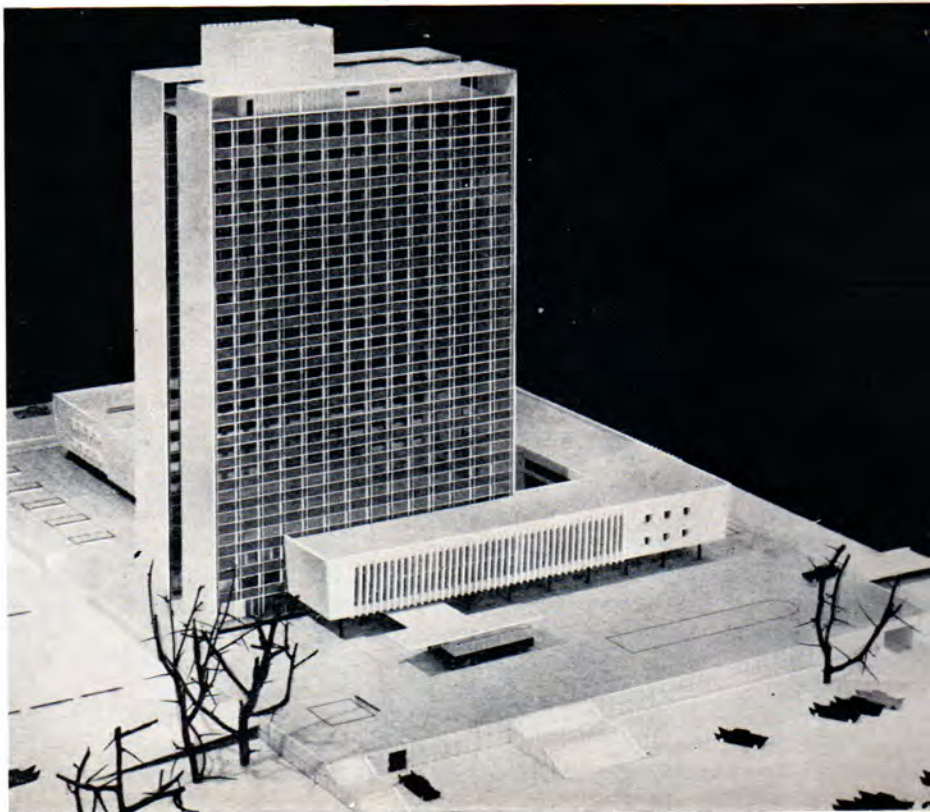

создать общегородской центр с общественными, спортивными, культурно-просветительными зданиями и сооружениями; использовать и развить прогрессивные методы типизации, сочетающие преимущества индустриального домостроения с архитектурным многообразием и высоким эстетическим качеством застройки. Для этого необходимо использовать дома различной протяженности, конфигурации и этажности, блокируемые из отдельных секций;


обеспечить защиту застройки от ряда неблагоприятных природно-климатических факторов.

В функциональном, планировочном и композиционном отношении массив застройки первой очереди является законченной структурной частью города, с развитым общегородским центром, полноценным культурно-бытовым обслуживанием, необходимой системой магистралей, с высоким уровнем озеленения, инженерного оборудования и благоустройства. Архитектурное решение и последовательность освоения первой очереди строительства обеспечивают ее органическое включение в планировочную структуру и композицию будущего города.

В район первой очереди входит значительная часть общегородского центра и наиболее живописная часть набережной.

Строительство центра города предусмотрено очередями. В первую очередь начнется строительство торгового центра и широкоформатного кинотеатра. Завершающий этап строительства—административный центр. В центре города зарезервированы территории для крупных зданий культурного назначения — цирка, концертного зала и др.

В композиционное решение центра включены также комплекс зданий вдоль Восточной магистрали перед фронтом 16-этажных жилых домов. Это крупные общественные здания общегородского назначения, которые будут дополнять всю систему обслуживания, сформируют общественно-

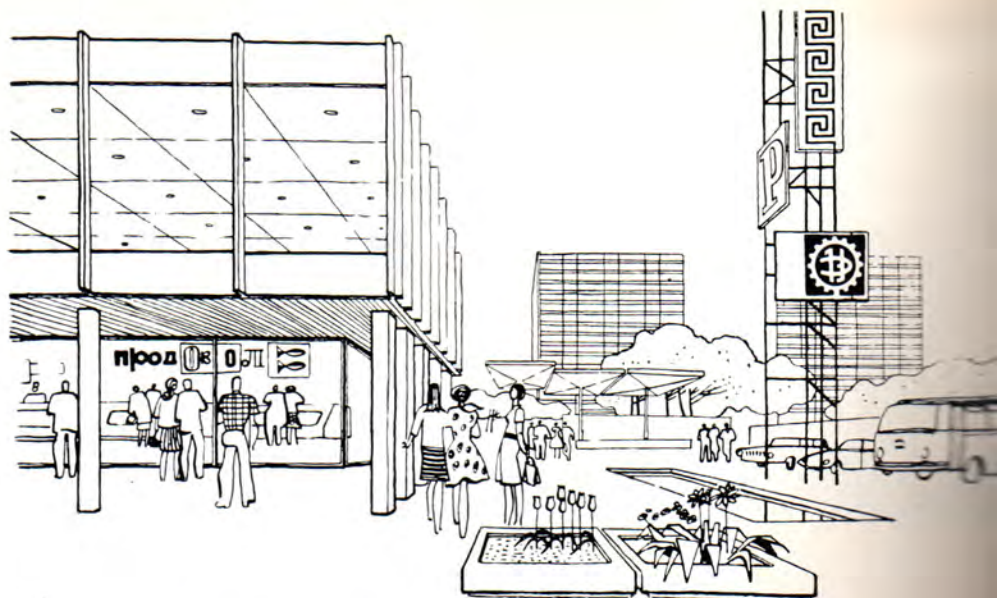

Микрорайонный центр. Перспектива

торговую улицу, являющуюся как бы началом центра всего города.

Жилая зона состоит из ряда районов, решенных по принципу укрупненных межмагистральных территорий площадью 90—100 га, включающих по два жилых микрорайона.

Площадь жилого района, в красных линиях, равна примерно 80 га, что позволяет создать жилой массив на 23—26 тыс. человек.

В жилых районах резервируются территории для открытых автостоянок и сооружаются подземные и полуподземные гаражи для легковых автомобилей индивидуального пользования.

Жилые районы расчленены улицами и пешеходными бульварами, соединяющими фокусные точки тяготения населения. Основные бульвары имеют ответвления к центрам обслуживания, расположенным у

остановок транспорта. Ширина основного бульвара 100 м, позволяет кроме аллей устраивать также места для отдыха, площадки для игр и спорта, достаточно удаленные от жилых комплексов.

К бульварам примыкают зеленые массивы, состоящие из участков школ и центрального спортивного ядра. В местах пересечения магистралей бульварами располагаются торговые и культурные центры районного значения. Для тихого отдыха создаются равномерно распределенные по всей территории, озелененные участки жилых групп.


Для удобства населения все центры районного и микрорайонного значения располагаются у остановок общественного транспорта. Наличие подземных переходов позволяет укрупнить центры обслуживания населения, что является предпосылкой улучшения их работ при снижении затрат на строительство и эксплуатацию.



Важными композиционными звеньями застройки являются жилые группы на 2—4 тыс. человек населения. Каждая группа располагается вокруг дворового участка площадью 1,5—2 га. При жилых группах размещаются здания яслей-детсадов.

Застройка предусматривается смешанной этажности (5, 9, 12 и 16 этажей), что позволяет обеспечить плотность жилого фонда 3600—3800 м² на 1 га территории и создать выразительное архитектурное решение.

В результате экономического и градостроительного анализа ряда вариантов застройки установлено следующее соотношение жилых домов по этажности: 5-этажный — 75%; 9—12 — 20% и 16 — 5%. Принятый в проекте удельный вес жилых домов повышенной этажности обеспечит значительный градостроительный эффект, при удорожании строительства в пределах 1,3—1,5%, по сравнению с 5-этажной застройкой.

Школа. Перспектива

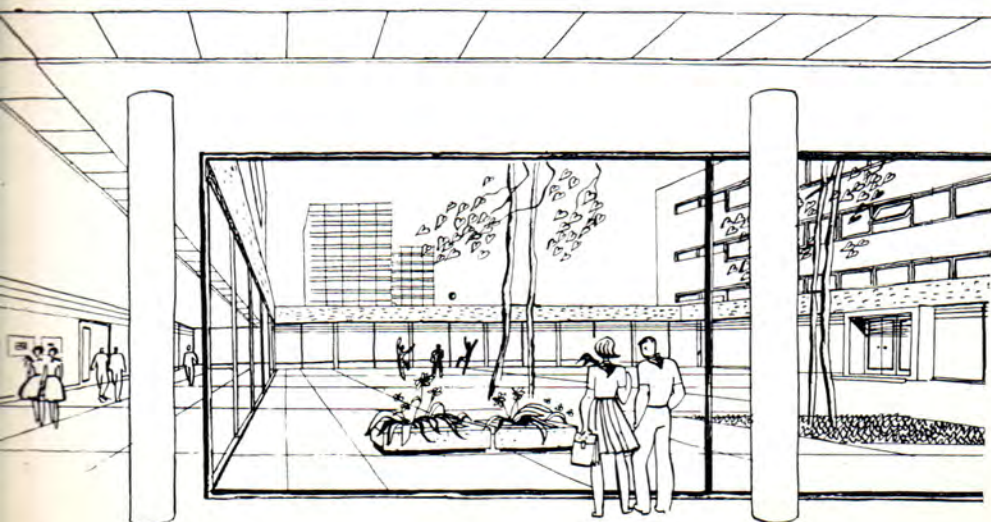

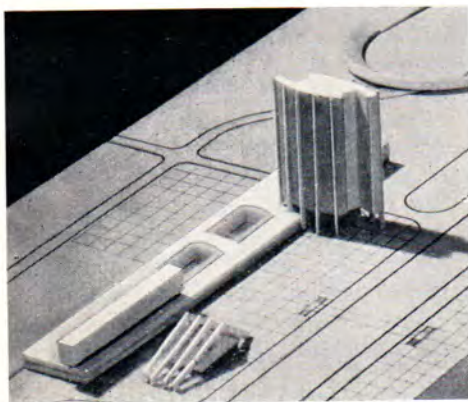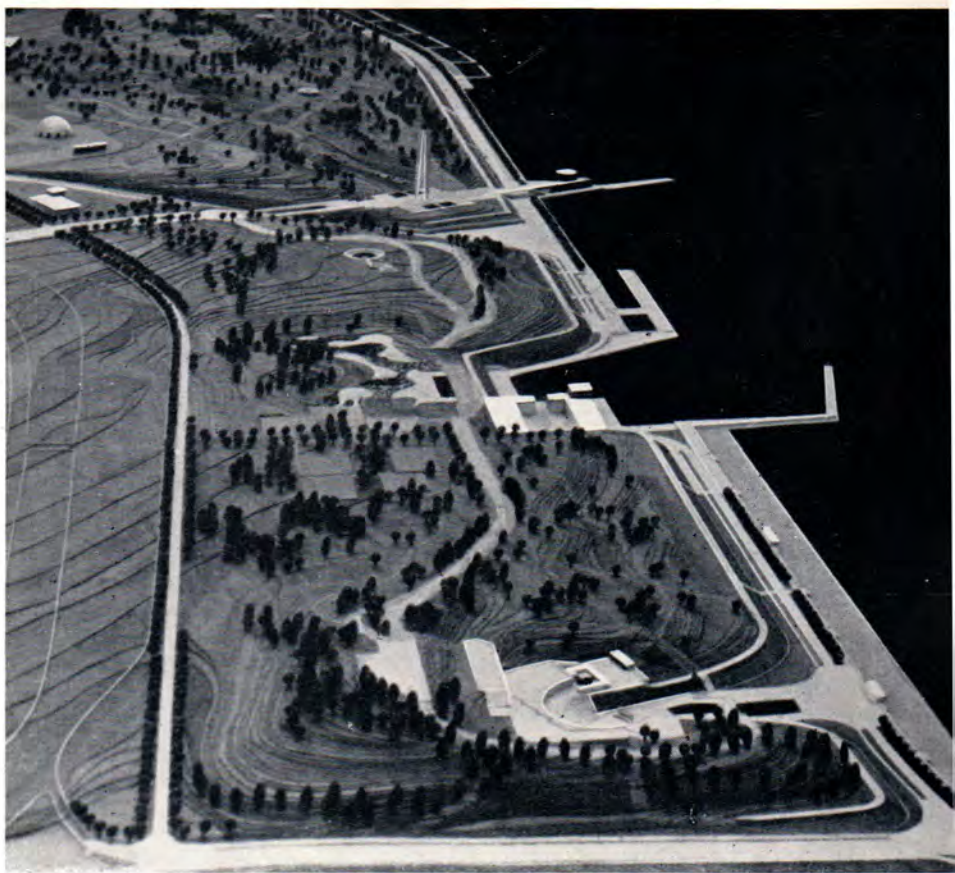

Площадь в предзаводском районе

С учетом эксплуатационных расходов (за срок окупаемости капитальных вложений 10 лет) и затрат на изъятие пропашных земель использование зданий повышенной этажности не приведет к удорожанию, по сравнению со сплошной 5-этажной застройкой.

Для расселения молодых рабочих и специалистов в 1967—1971 гг. вдоль бульвара Север — Юг будут построены дома с улучшенной планировкой и повышенными удобствами заселения. Дома для мало-семейных представляют собой комплекс жилых зданий и блока культурно-бытового обслуживания. В комплекс, рассчитанный на 3000 чел., входят два жилых здания высотой 9 и 12 этажей с отдельными жилыми ячейками, поэтажными гостиницами и вестибюлями. В перспективе намечено строительство 20-этажных домов для мало-семейных.

Сильные зимние ветры, дующие со стороны водохранилища, вызывают необходимость создавать в жилых группах полузакрытые обширные дворы различной протяженности и конфигурации и размещать детские учреждения в зоне ветровой тени. Разработаны проекты жилых групп, состоящих из нескольких типов блокируемых домов и угловых секций, что при больших расстояниях между фасадами (до 100 м) дало высокие экономические показатели. В проекте обеспечены оптимальные условия инсоляции жилых помещений и их зрительная изоляция. При решении застройки вдоль магистралей ставилась задача создать индивидуальный архитектурный облик каждой улицы.

Строительство объектов культурно-бы-

тового назначения и коммунального хозяйства, основных транспортных магистралей, инженерных сооружений, медицинского центра и спортивного комплекса будет осуществляться раньше возведения жилых домов.

Квартиры в различных типах домов имеют высоту 2,7 м. Они оборудованы встроенными шкафами хозяйственного назначения, стационарной кухонной мебелью и другими современными предметами бытового обихода. Особое внимание было уделено качеству внутренней отделки квартир, столярных изделий, оконных и дверных приборов, благоустройству лестничных клеток, вестибюлей и входов.

Новый город Тольятти должен быть построен в ускоренные сроки, а автозавод выпустить первые автомашины уже в 1967 г. с выходом на полную мощность в 1970 г. В течение пяти лет (до 1972 г.) предстоит построить новый город с населением 150—160 тыс. человек.

В связи с такими быстрыми темпами строительства автомобильного завода и всего комплекса возникла необходимость в самые короткие сроки обеспечить весь комплекс строительства; по новому организовать разработку, выдачу проектной документации и использовать новые методы решения градостроительных вопросов.

Опыт комплексного проектирования и четкой организации строительства новой части города Тольятти может представлять интерес для широкого круга градостроителей и архитекторов, работающих над проблемами строительства и развития новых городов.